


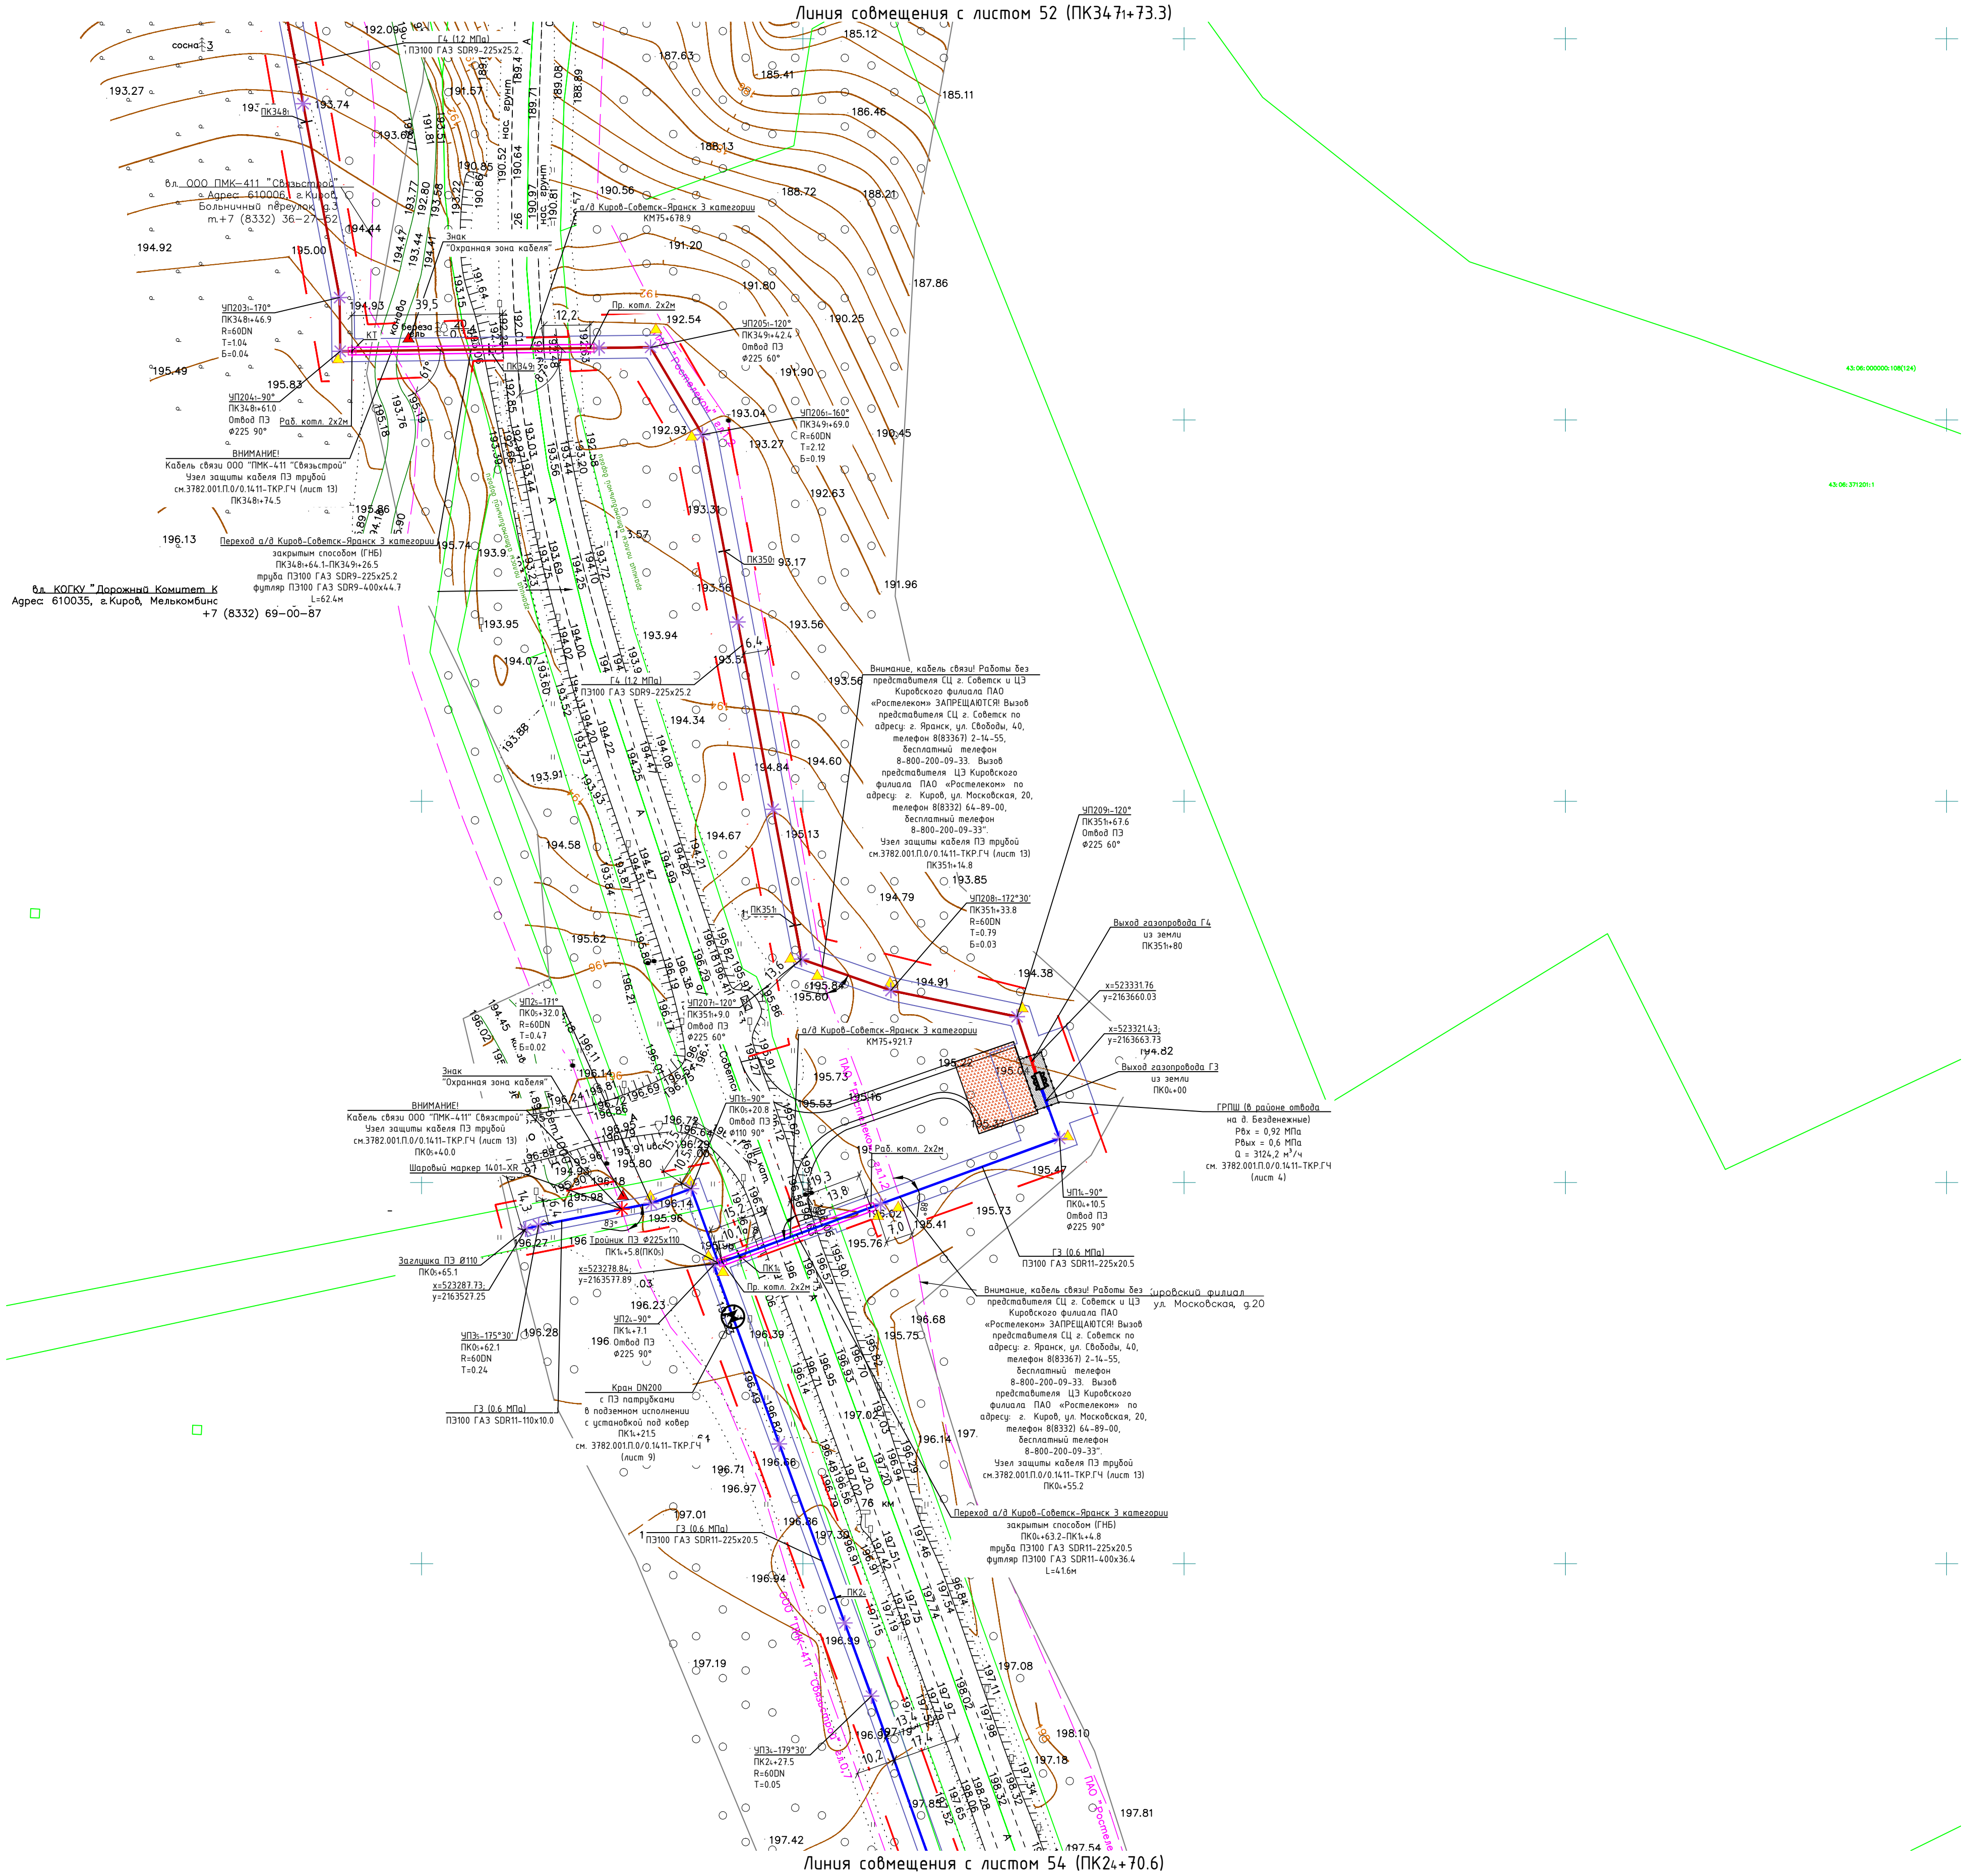


Схема расположения листов

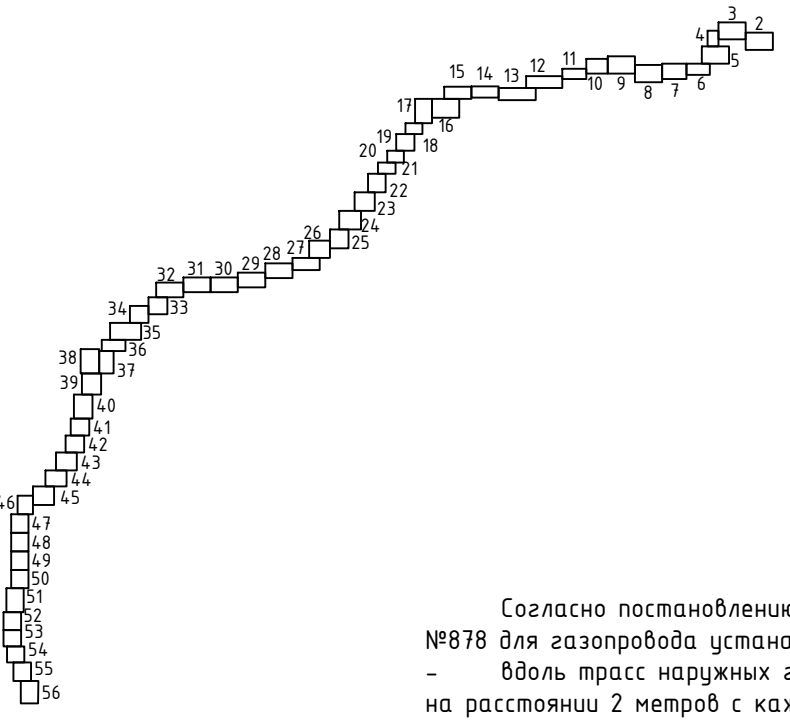

Согласно постановлению «Об утверждении Правил охраны газораспределительных сетей» от 20.11.2000г.
№878 для газопровода устанавливается охранная зона:
- вдоль трасс наружных газопроводов - в виде территории, ограниченной условными линиями, проходящими на расстоянии 2 метров с каждой стороны газопровода;
- вдоль трассы межселового газопровода, проходящего по лесам и древесно-кустарниковой растительности, - в виде просек шириной 6 метров, по 3 метра с каждой стороны газопровода;
- вокруг отдельно стоящего газорегуляторного пункта - в виде территории, ограниченной замкнутой линией, проведенной на расстоянии 10 метров от границ этих объектов.

- Условные обозначения:
- газопровод высокого давления 1 категории;
 - газопровод высокого давления 2 категории;
 - граница охранных зон;
 - граница полосы отвода;
 - монтажный котлован размером 2х2м;
 - опознавательный столбик;
 - пассивный шпильный маркер;
 - контрольная трубка;
 - футляр газопровода;
 - придорожно защитная полоса (ПЗП);
 - водоохранная зона (ВОЗ);
 - граница населенного пункта;
 - граница полосы отвода автомобильной дороги

Координаты углов		
Номер угла	x	y
УП203н	523532.12	2163478.49
УП204н	523518.05	2163478.66
УП205н	523519.05	2163560.04
УП206н	523496.15	2163573.64
УП207н	523358.59	2163599.65
УП208н	523350.39	2163623.09
УП209н	523343.48	2163656.18
УП1н	523311.53	2163667.34
УП2н	523278.39	2163576.65
УП3н	523165.3	2163617.99
УП5н	523298.38	2163570.75
УП2с	523294.55	2163560.25
УП3с	523288.76	2163530.68

XXXX-ППО.ГЧ				
Газопровод межселовый от д. Кучелаты Оршанского района - лпм. Верхошские с отводом на д. Пучино, с. Игасан и отключающим устройством на д. Безденежные Верхохвостского района Кировской области				
Изм.	Кол.уч.	Лист	№ док.	Подпись
Разработал	Размечал			
Проверил				
Н.контр.				
Проект полосы отвода		Студия	Лист	Листов
План газопровода		п	53	
ПКС47+73.3-ПКС35+78.0; ПКО-ПКС2+70.6; ПКО-ПКО+65.1; М11000				