
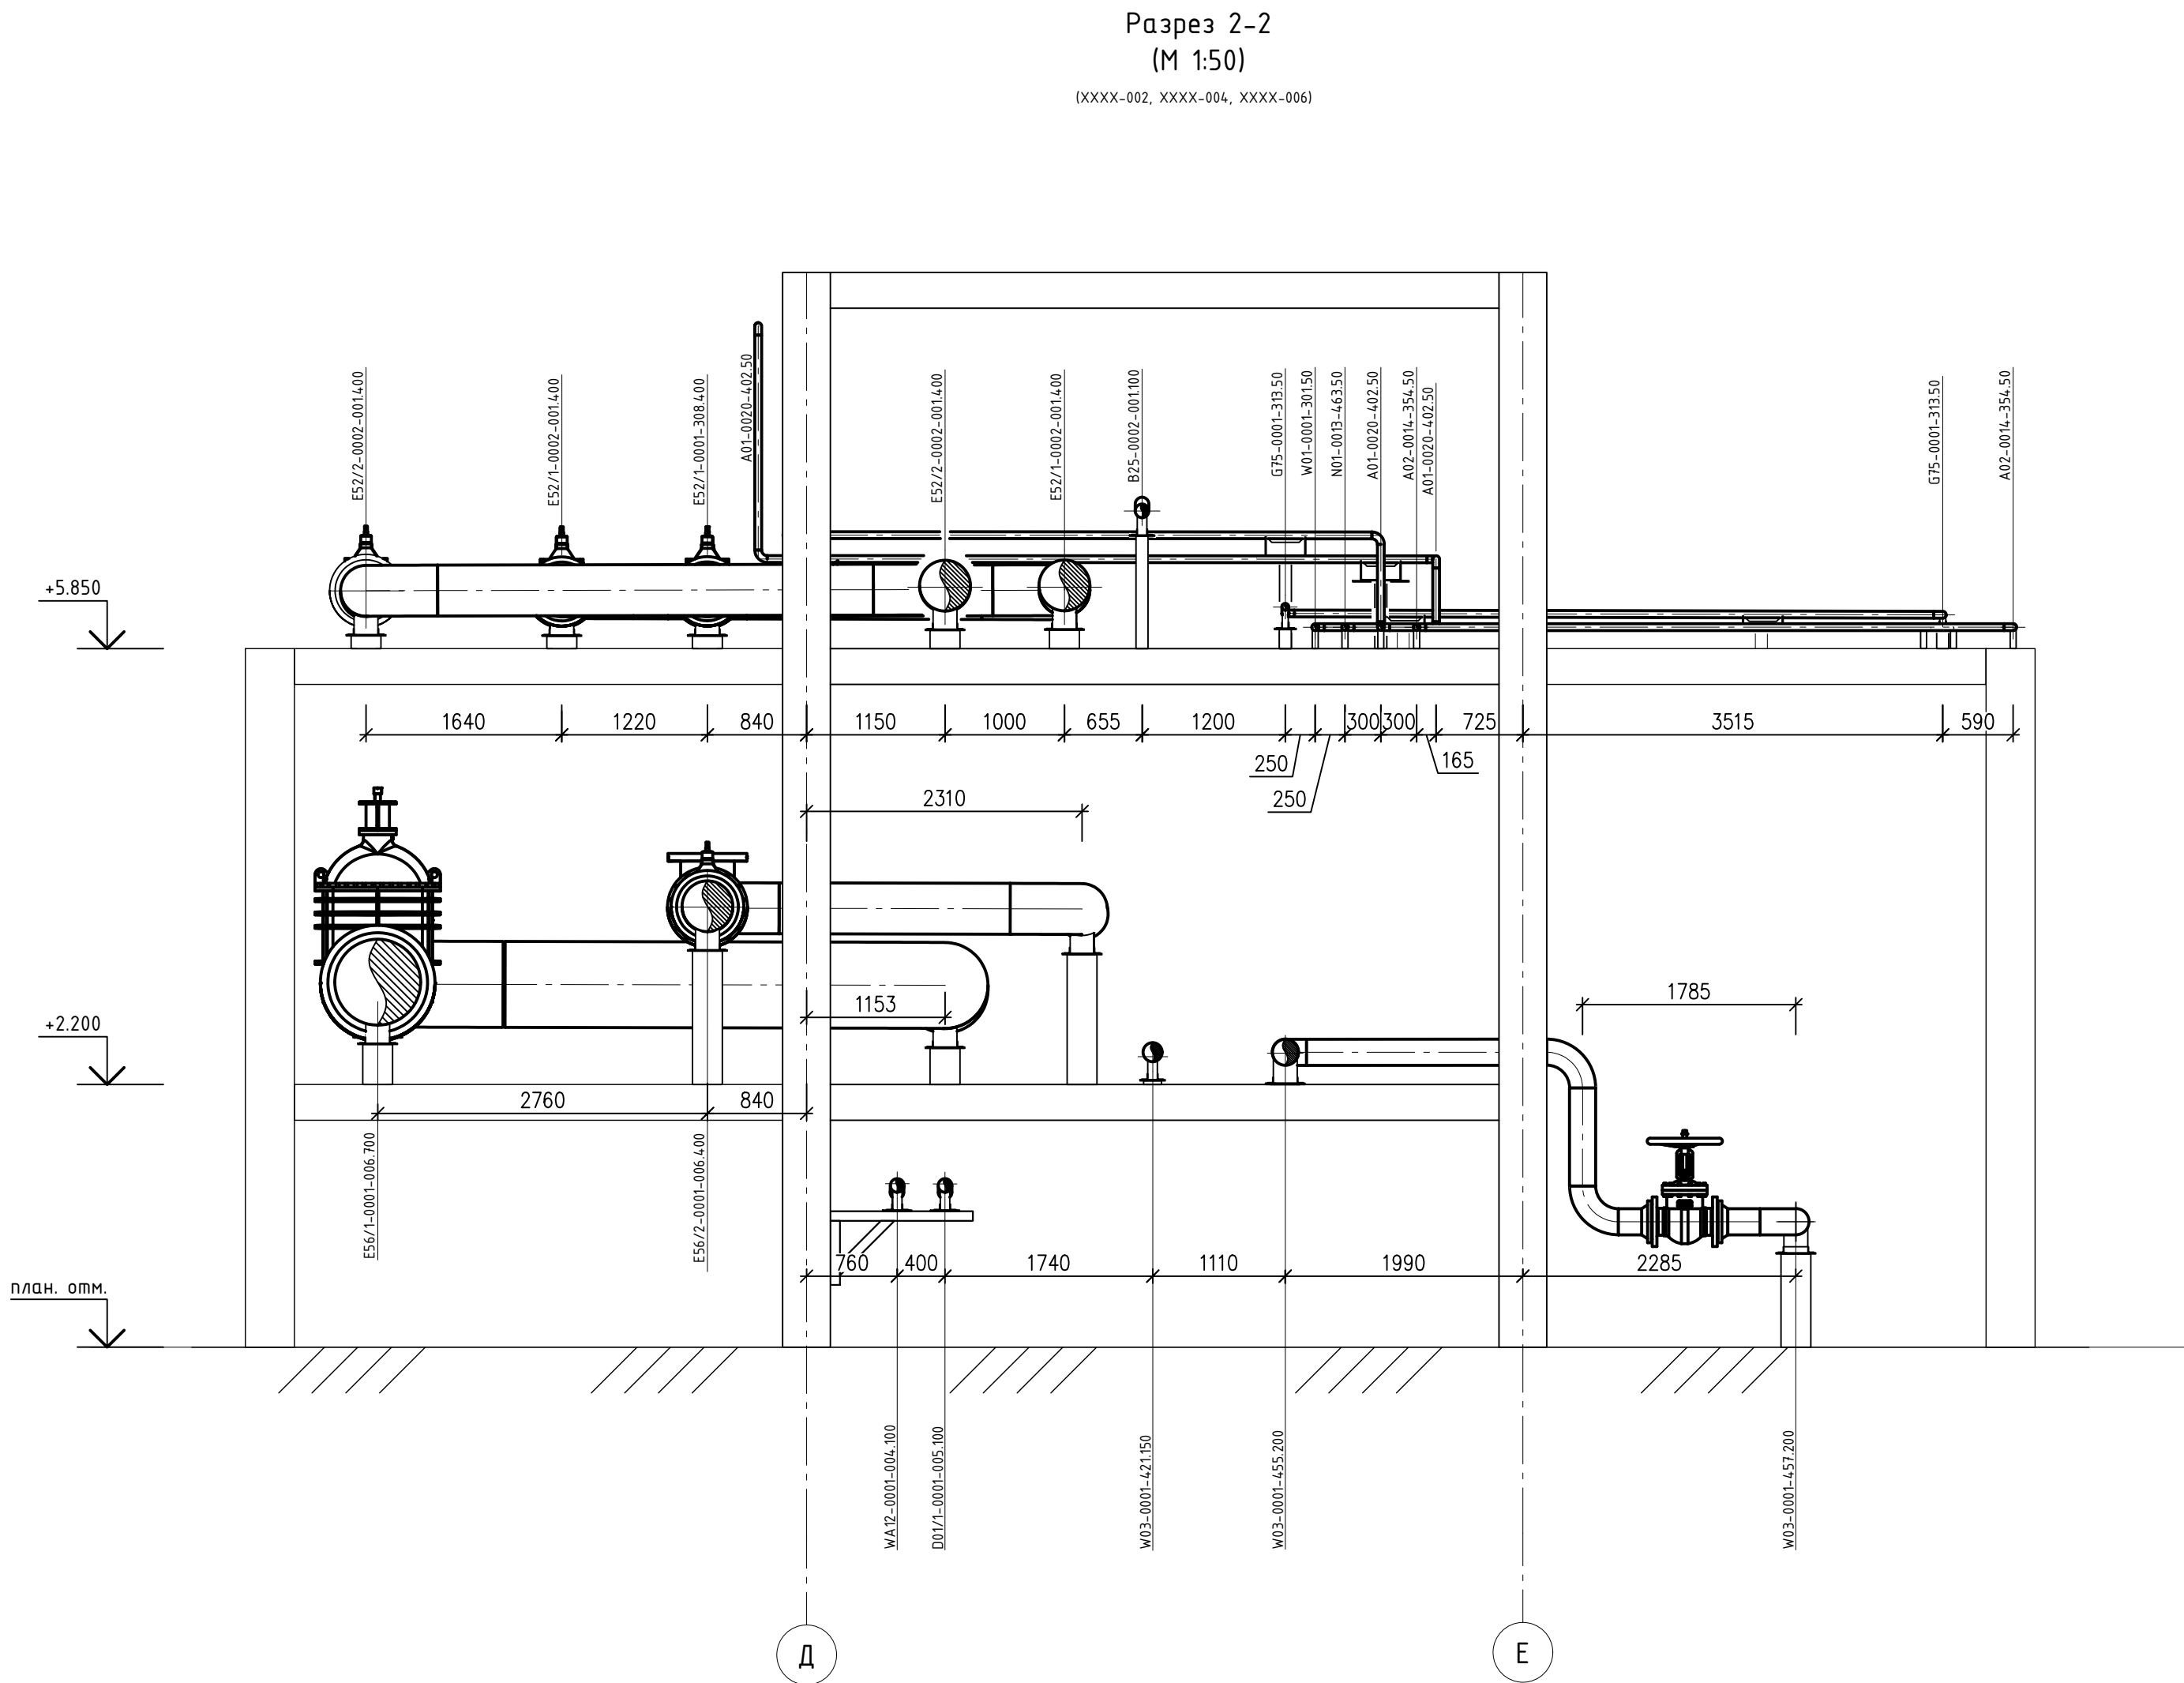
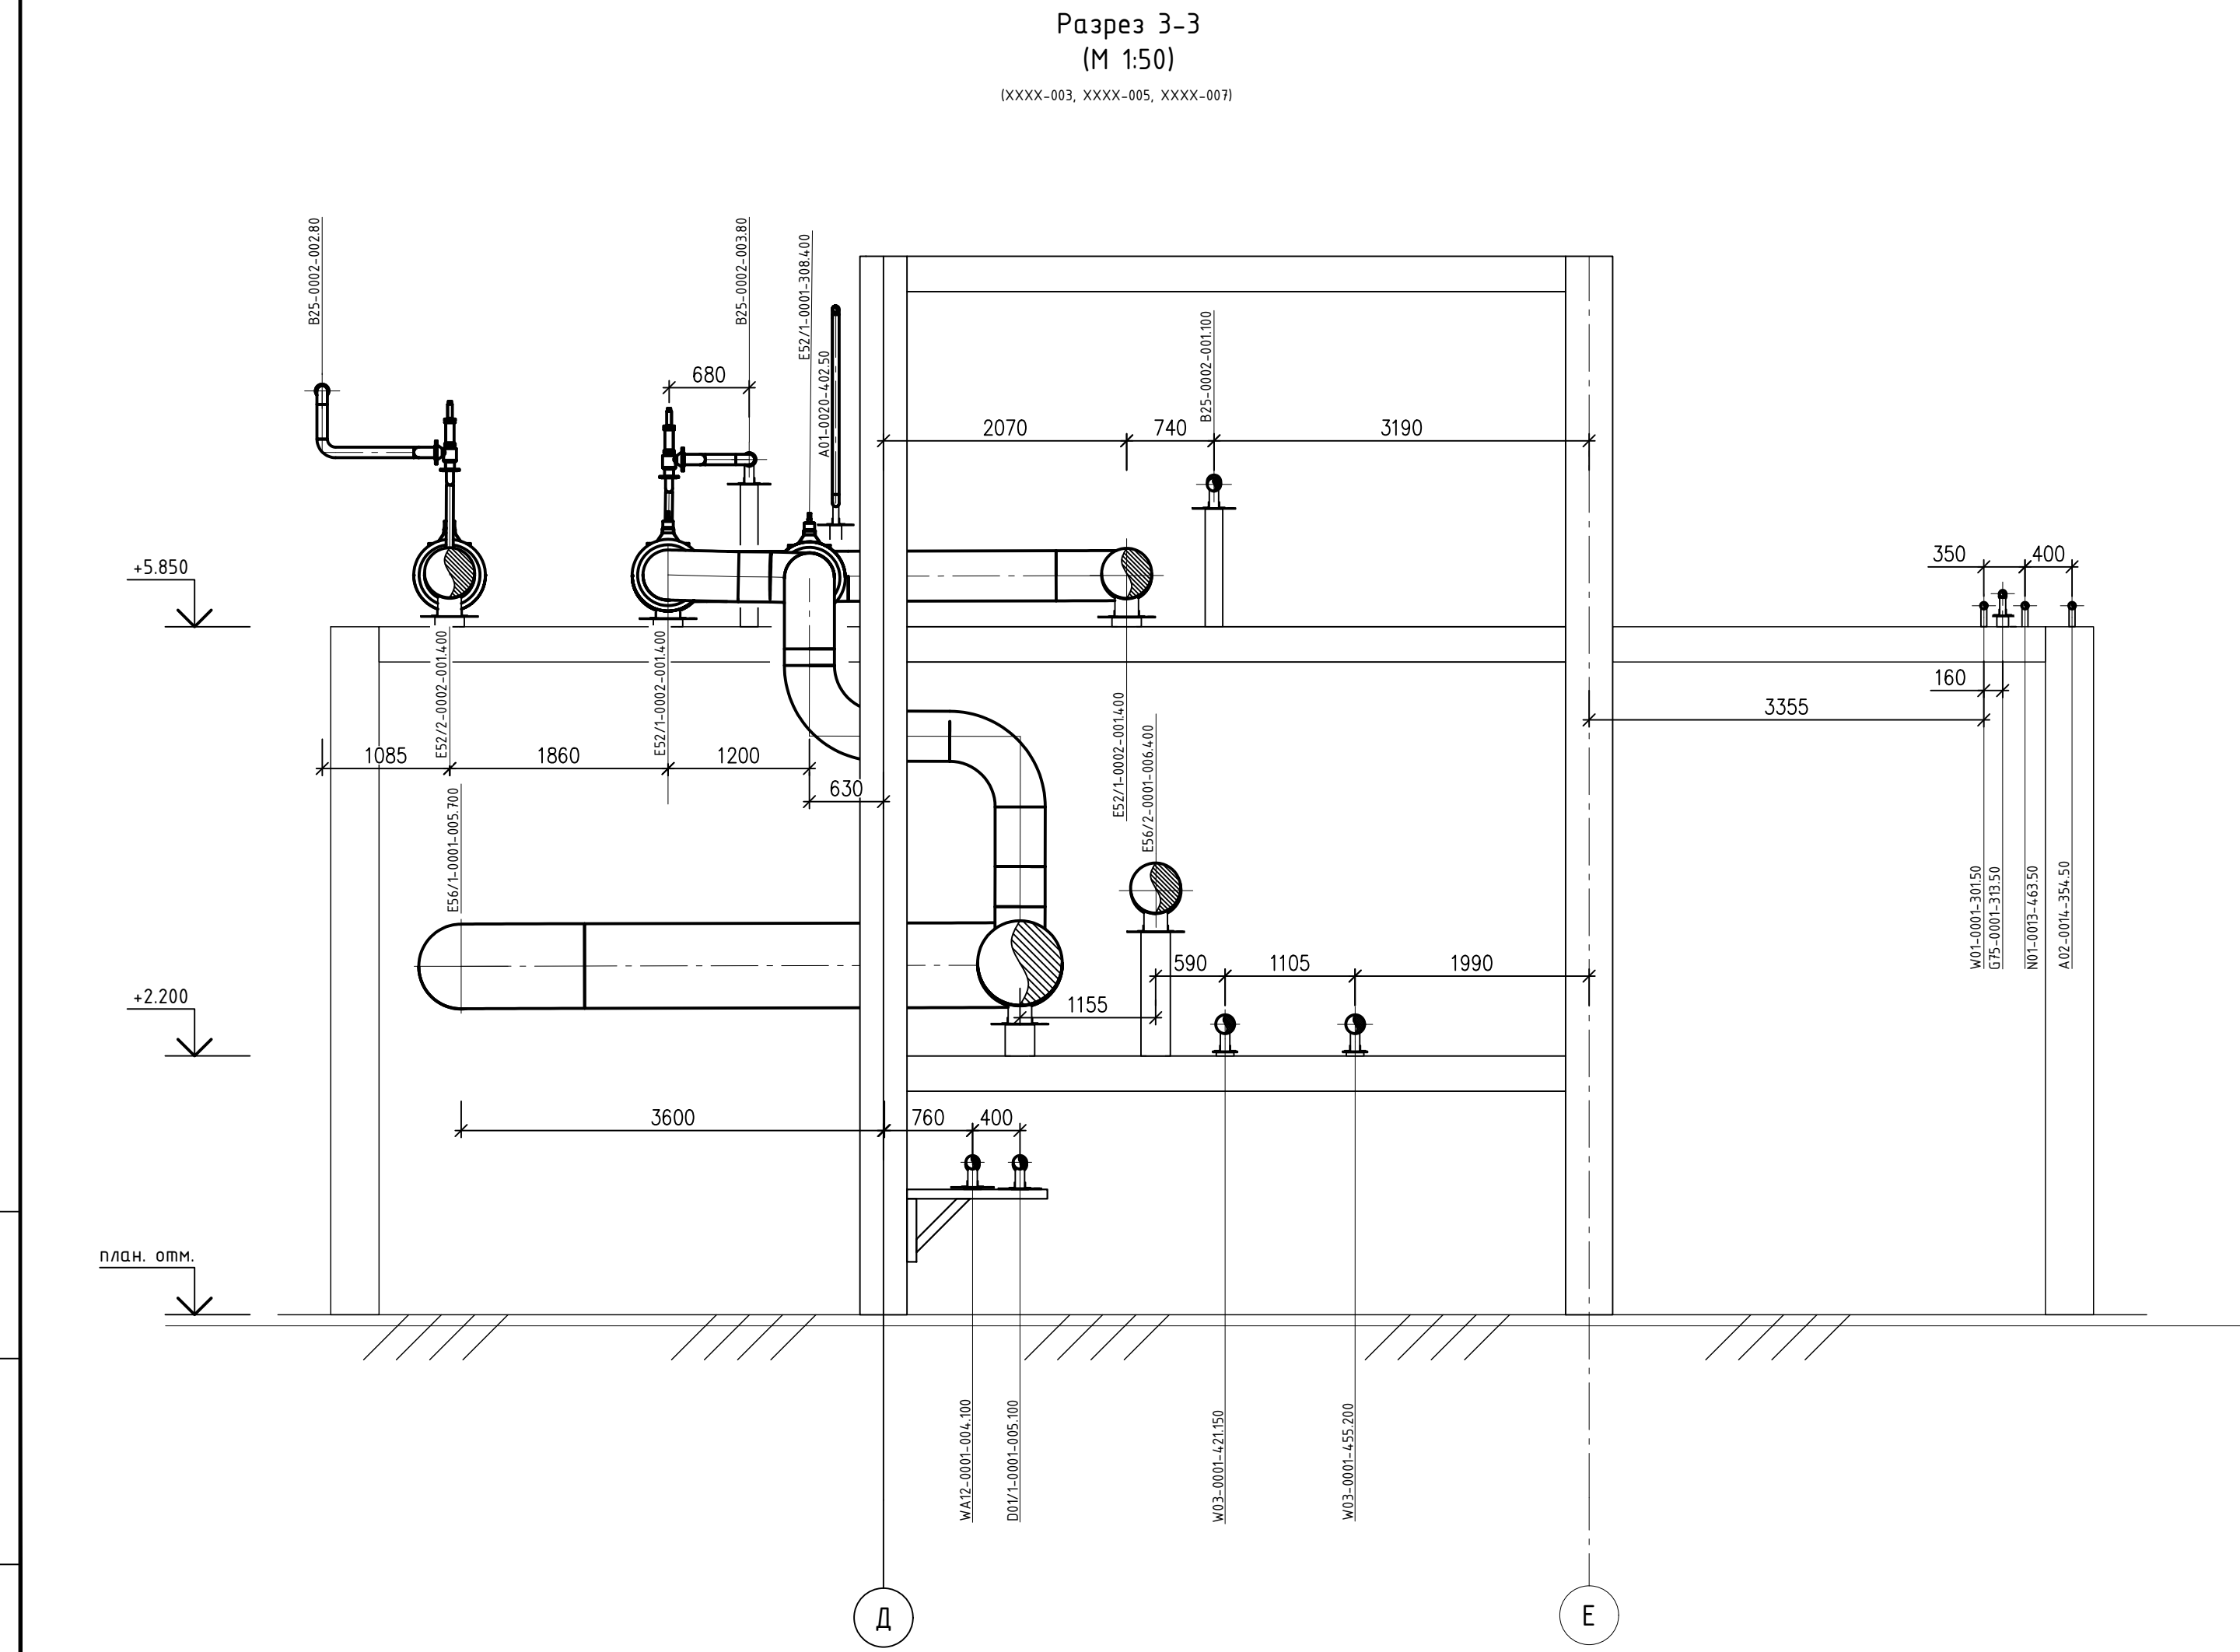


Вариант шифра	Вариант шифра
Подпись и дата	Подпись и дата
Имя, И.И.П.	Имя, И.И.П.

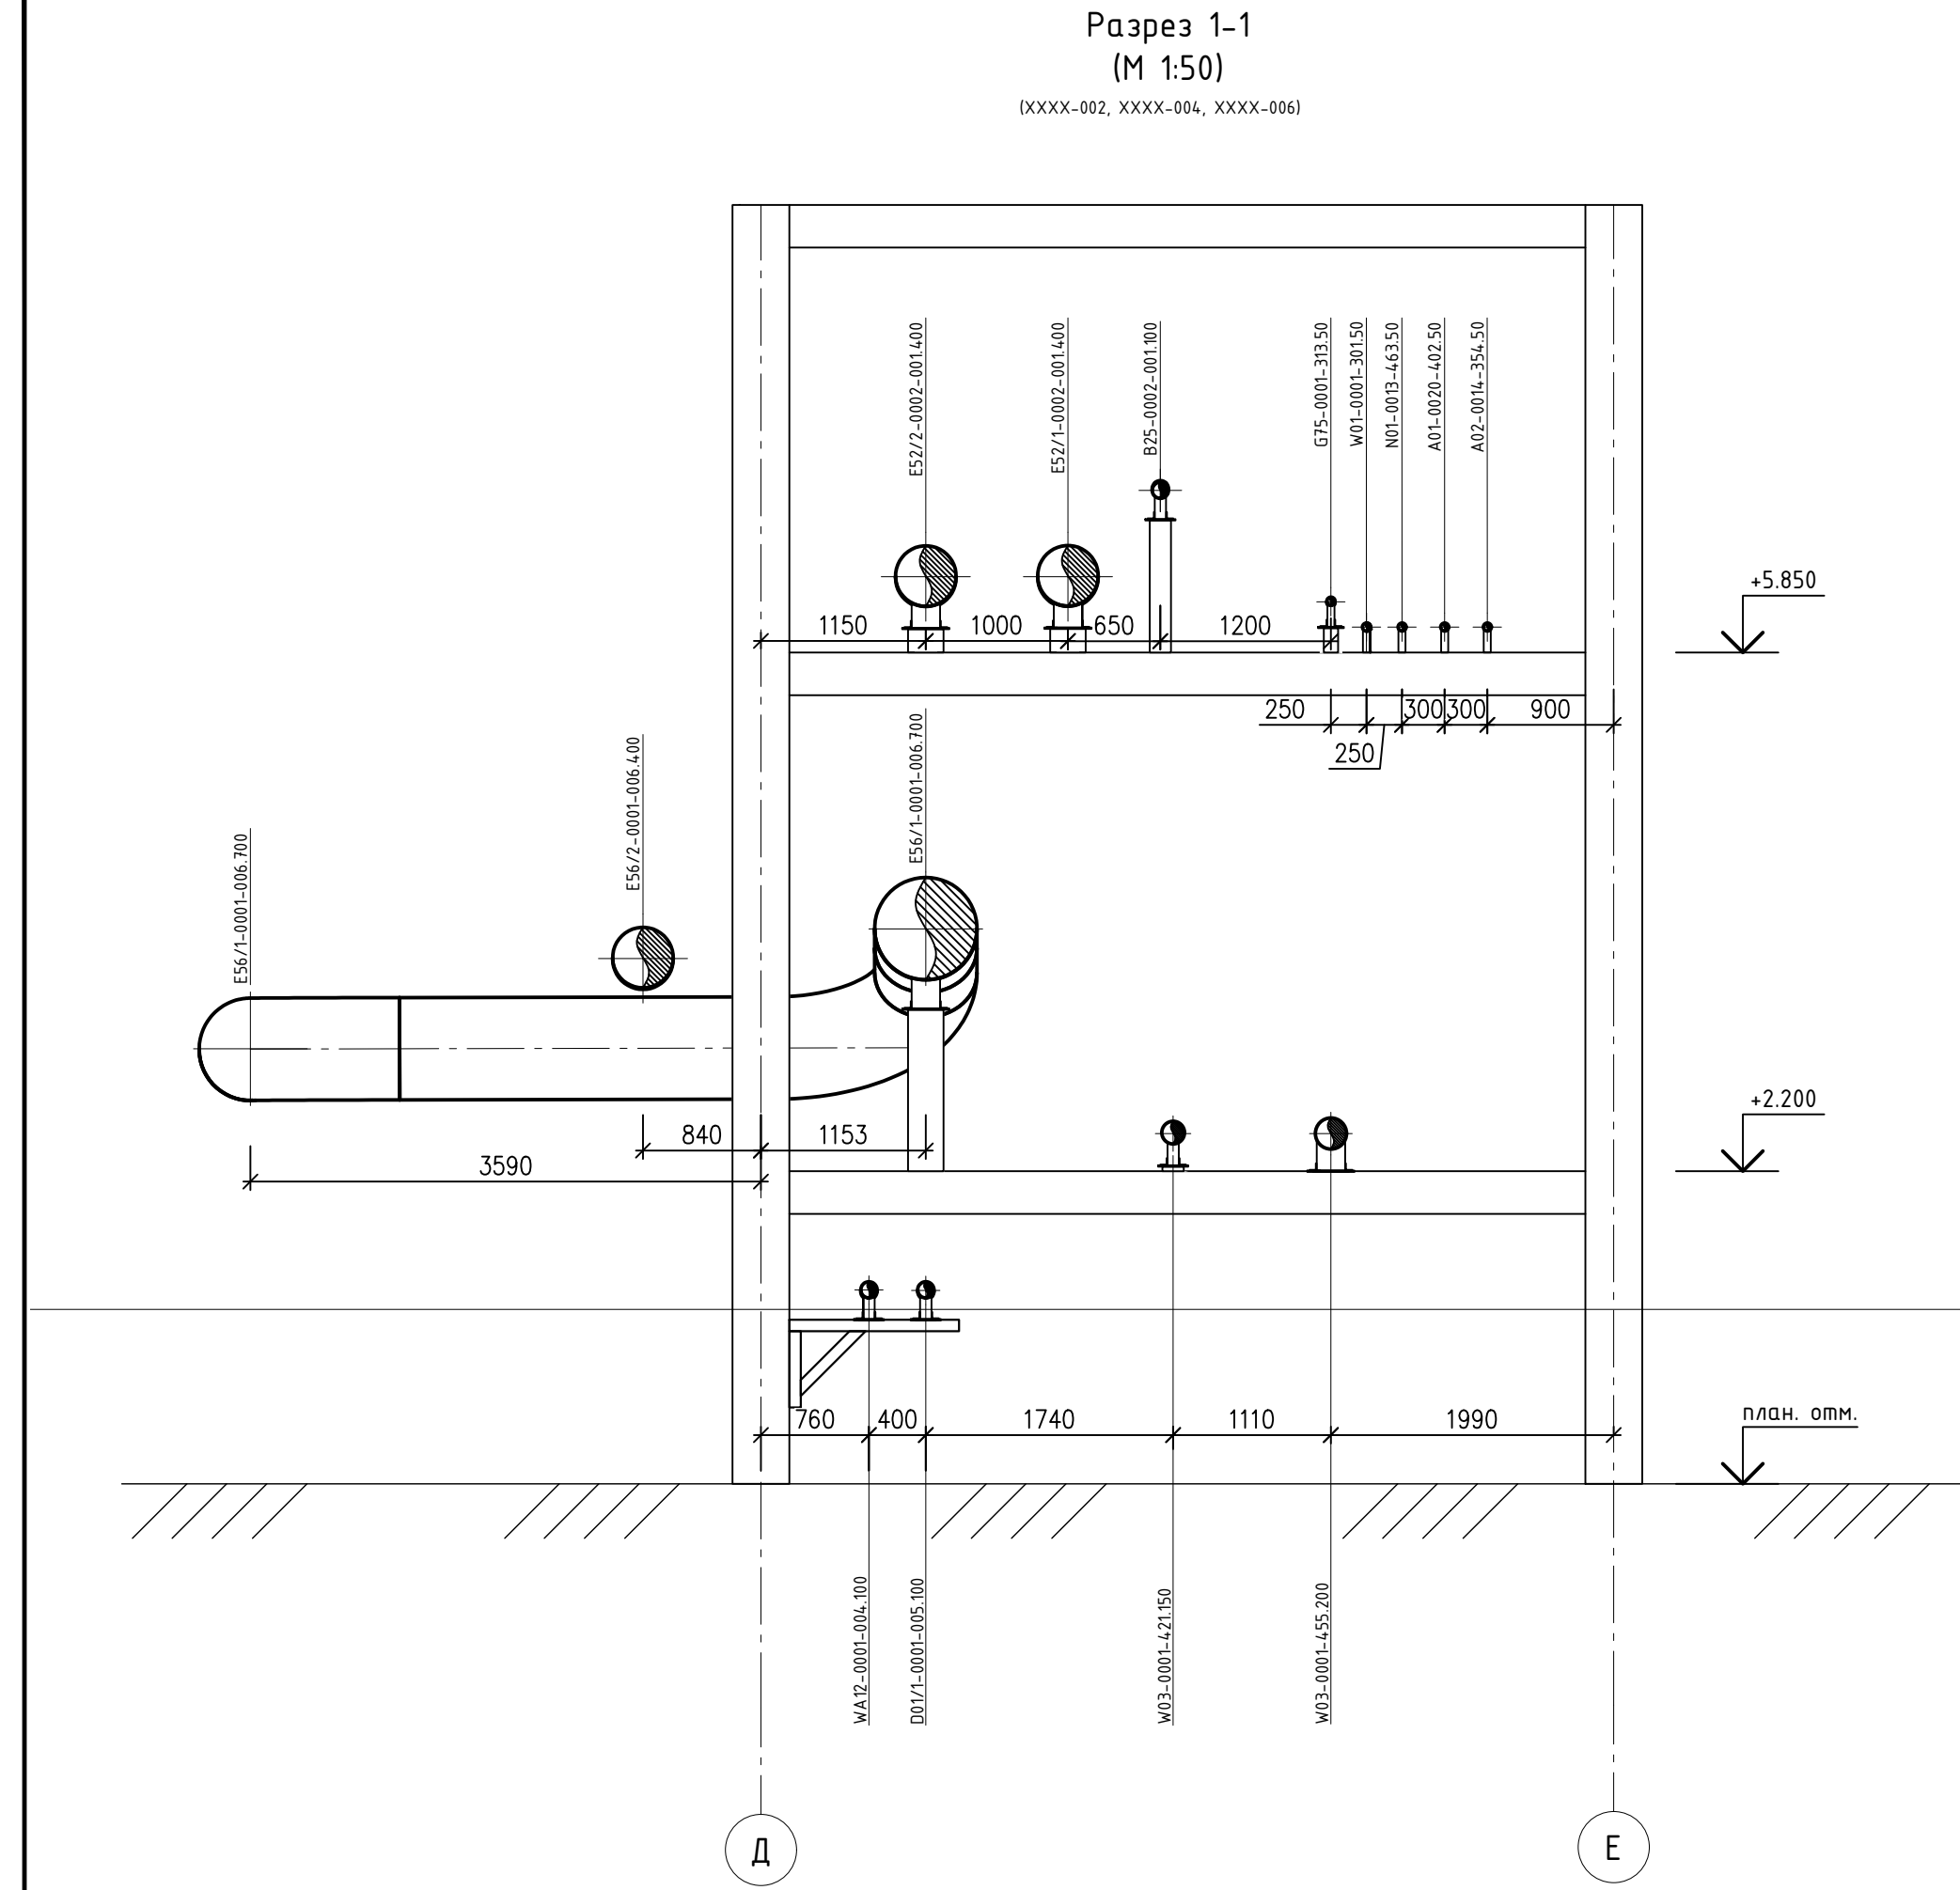

- Условные обозначения
- 1 — Ось строительных конструкций
1. Данный чертеж рассматривать совместно с XXXX-002, XXXX-007
2. Строительные конструкции показаны условно.
3. За относительную отметку 0,000 терминала отгрузки ЖУВ и СУГ принята абсолютная отметка 7,000.

							XXXX-008
							Бованенковское нефтегазоконденсатное месторождение. Терминал отгрузки ЖУВ и СУГ
Изм.	Колуч.	Лист	№ док.	Подпись	Дата		
Разработал						Эстакада №7 (итог. 3.10)	Стадия
Проверил							Лист
							Листов
Н.контр.						Разрезы 1-1, 2-2, 3-3	
Гип							