


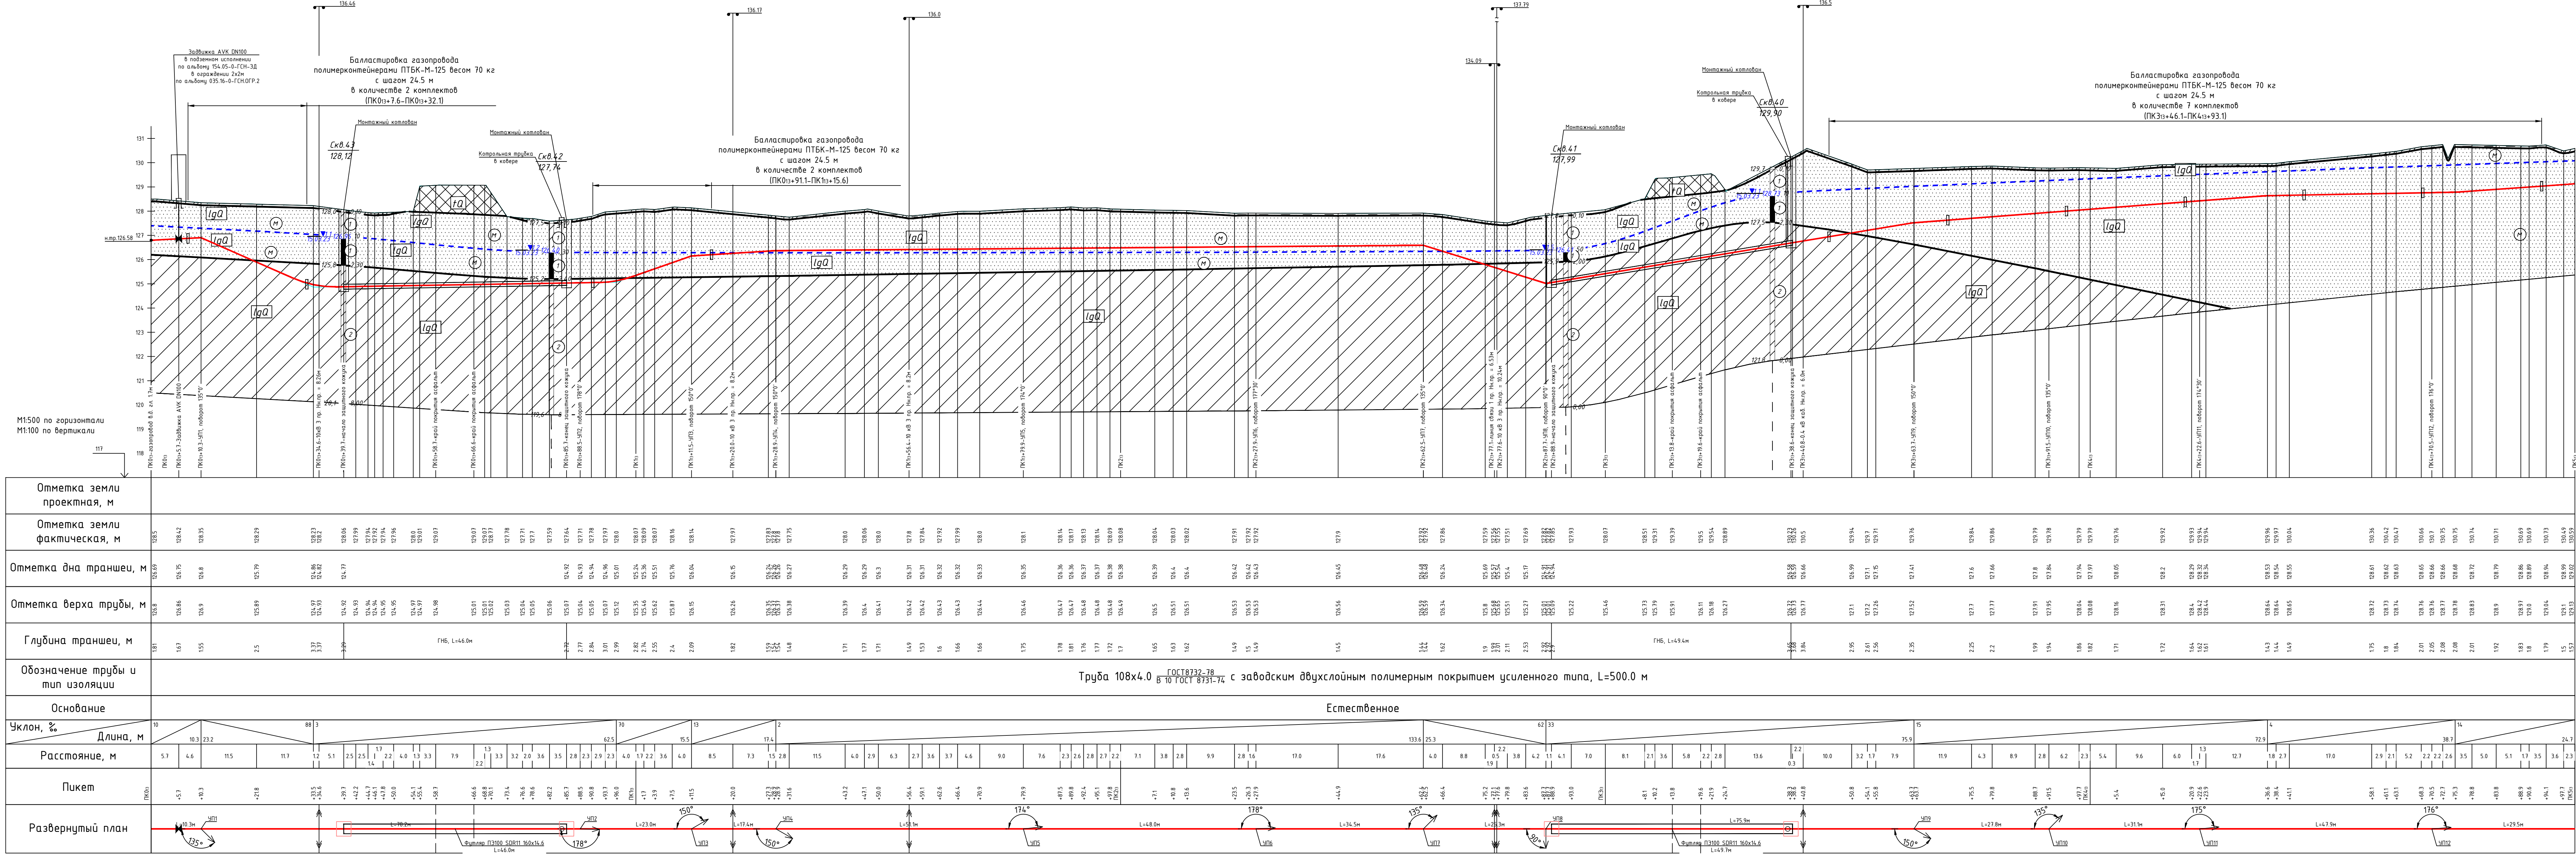

XXXX-ППО.ГЧ			
«Газопровод высокого давления к д. Лудино с последующей газификацией» городского округа Воскресенск Московской области			
Изм.	Кол.	Лист № док.	Подпись
Разработал	Разиньков		
Проверил			
Проект полосы отвода		Стадия	Лист
		П	13
Н.контр.		Продольный профиль газопровода ПК0+00-ПК5+00	