




Экспликация оборудования			
Обознач.	Наименование	Кол-во	Примечание
НГС-1, 2	Нефтезащитный сепаратор со сбросом воды объемом 25 м³, РН 1,0 МПа	2	НГС-Н-1,0-2000-2-И
НГС-3	Нефтезащитный сепаратор объемом 50 м³, РН 1,0 МПа	1	НГС-Н-1,0-2400-2-И
БЕ-1, 2	Буферная емкость объемом 100 м³, РН 1,0 МПа	2	ОГВ-100-3000
ЦНС-1, 2	Насос центробежный секционный с расходом 180 м³/час и напором 383 м	2	ЦНСМ-180-383
ФЖ-1, 2	Фильтр жесткости универсальный DN150	2	ФЖУ-150-1,6
КЗОВ	Камера приема очистных устройств	3	
КЗОВ	Камера загрузки очистных устройств	1	
ОГ-1, 2	Оптический горизонтальный нефть с перегородками объемом 180 м³, РН 1,0 МПа	2	ОГН-П-180-1,0-2
ОГ-3	Оптический горизонтальный нефть с перегородками объемом 200 м³, РН 1,0 МПа	1	ОГН-П-200-1,0-2
ОБ-1, 2	Оптический горизонтальный вода шифробойный объемом 200 м³, РН 1,0 МПа	2	ОГВ-П-200-1,0-2
Н-1, 2	Потопный насос канальный горизонтальный с расходом 360 м³/час и напором 80 м	2	НВБ 360/80 А-С-СД-12
Ф-1, 2	Фильтр сетчатый Y-образный DN300	2	ФС-300
Н-3, Н-5	Насос проточный для платовой воды с расходом 1674 м³/сут и максимальным рабочим давлением 15,0 МПа	3	СНН 61
Ф-3, Ф-5	Фильтр сетчатый Y-образный DN200	3	ФС-200
С-3, С-5	Расширитель с КМН и индикатором	3	ДРС МН-250-25-П-1,5
Н-6, 7	Насос фекальный буровой с максимальным давлением на входе 15 МПа и поворот 32 м³/час	2	НБ-125
Ф-6, 7	Фильтр жесткости универсальный DN150	2	ФЖУ-150-1,6
Н-8	Установка аэрирования шнекового насоса с расходом 25 м³/час и напором 18 м	1	УОДН 130-100-75 3БУТ
Ф-8	Фильтр сетчатый Y-образный DN150	1	ФС-150
С-1, 2	Расширитель с КМН и индикатором	2	ДРС МН-200-25-П-1,5
ЕД-1	Емкость производственного стока V=200 м³	1	ЕП-200-3400
НГ-1	Агрегат электронасосный полупроводниковый с поворот 80 м³/час и напором 4,3 м	1	12НА-9-И-4760-А-У
ЕД-2	Емкость производственного стока V=5 м³	1	ЕП-5-1600
НБ-1, 2	Агрегат электронасосный полупроводниковый производительность 3 м³/ч и напором 32 м	2	ВНД 3/32
НБ-3, 4, 5	Агрегат электронасосный полупроводниковый производительность 50 м³/ч и напором 50 м	3	НБ 50/50
ЕД-3	Емкость паровая дренажная объемом 5 м³ Рроб. 0,07 МПа	1	ЕП 5-1600
Н-9	Полупроводниковый насос ВНД 12,5/12,5	1	ВНД 12,5/12,5
КНЗ	Емкость конденсата V=5 м³	1	ЕП-5-1600
КЗЗ	Емкость конденсата V=25 м³	1	ЕП-25-2400
БР-1, 3	Блок дозирования ингибитора коррозии	2	БДР-10
БР-2	Блок дозирования регулятора	1	БДР-10
БНС	Блочная установка насосная станция	1	
Ф	Факельная установка	1	
УР	Установка рекуперативная	1	
БРП	Блок рекуперации газа факельной установки	1	
БВТ	Блок утилизации топливным газом рекуперативной установки	1	
БНРУ	Блок насоса рекуперативной установки	1	
БПБ	Блок пропан-бутановых баллонов	1	
ПНВ	Пункт налива воды	1	
УГ-1	Узел учета газа высокого давления на факельную установку	1	
УГ-2	Узел учета газа высокого давления на рекуперативную установку	1	
УГ-3	Узел учета газа низкого давления на факельную установку	1	
УГ-4	Узел учета топливного газа	1	
УГ-5	Узел учета воды на рекуперативную установку	1	

XXXXXXXXXXXX-И07.2			
Объект: Окуневское м.п. Второй этап			
Изм.	Кол-во	Лист	Дата
Резерв			
Генпр.			
Инженер			
Технологическая схема		Содерж.	Лист
		п	19