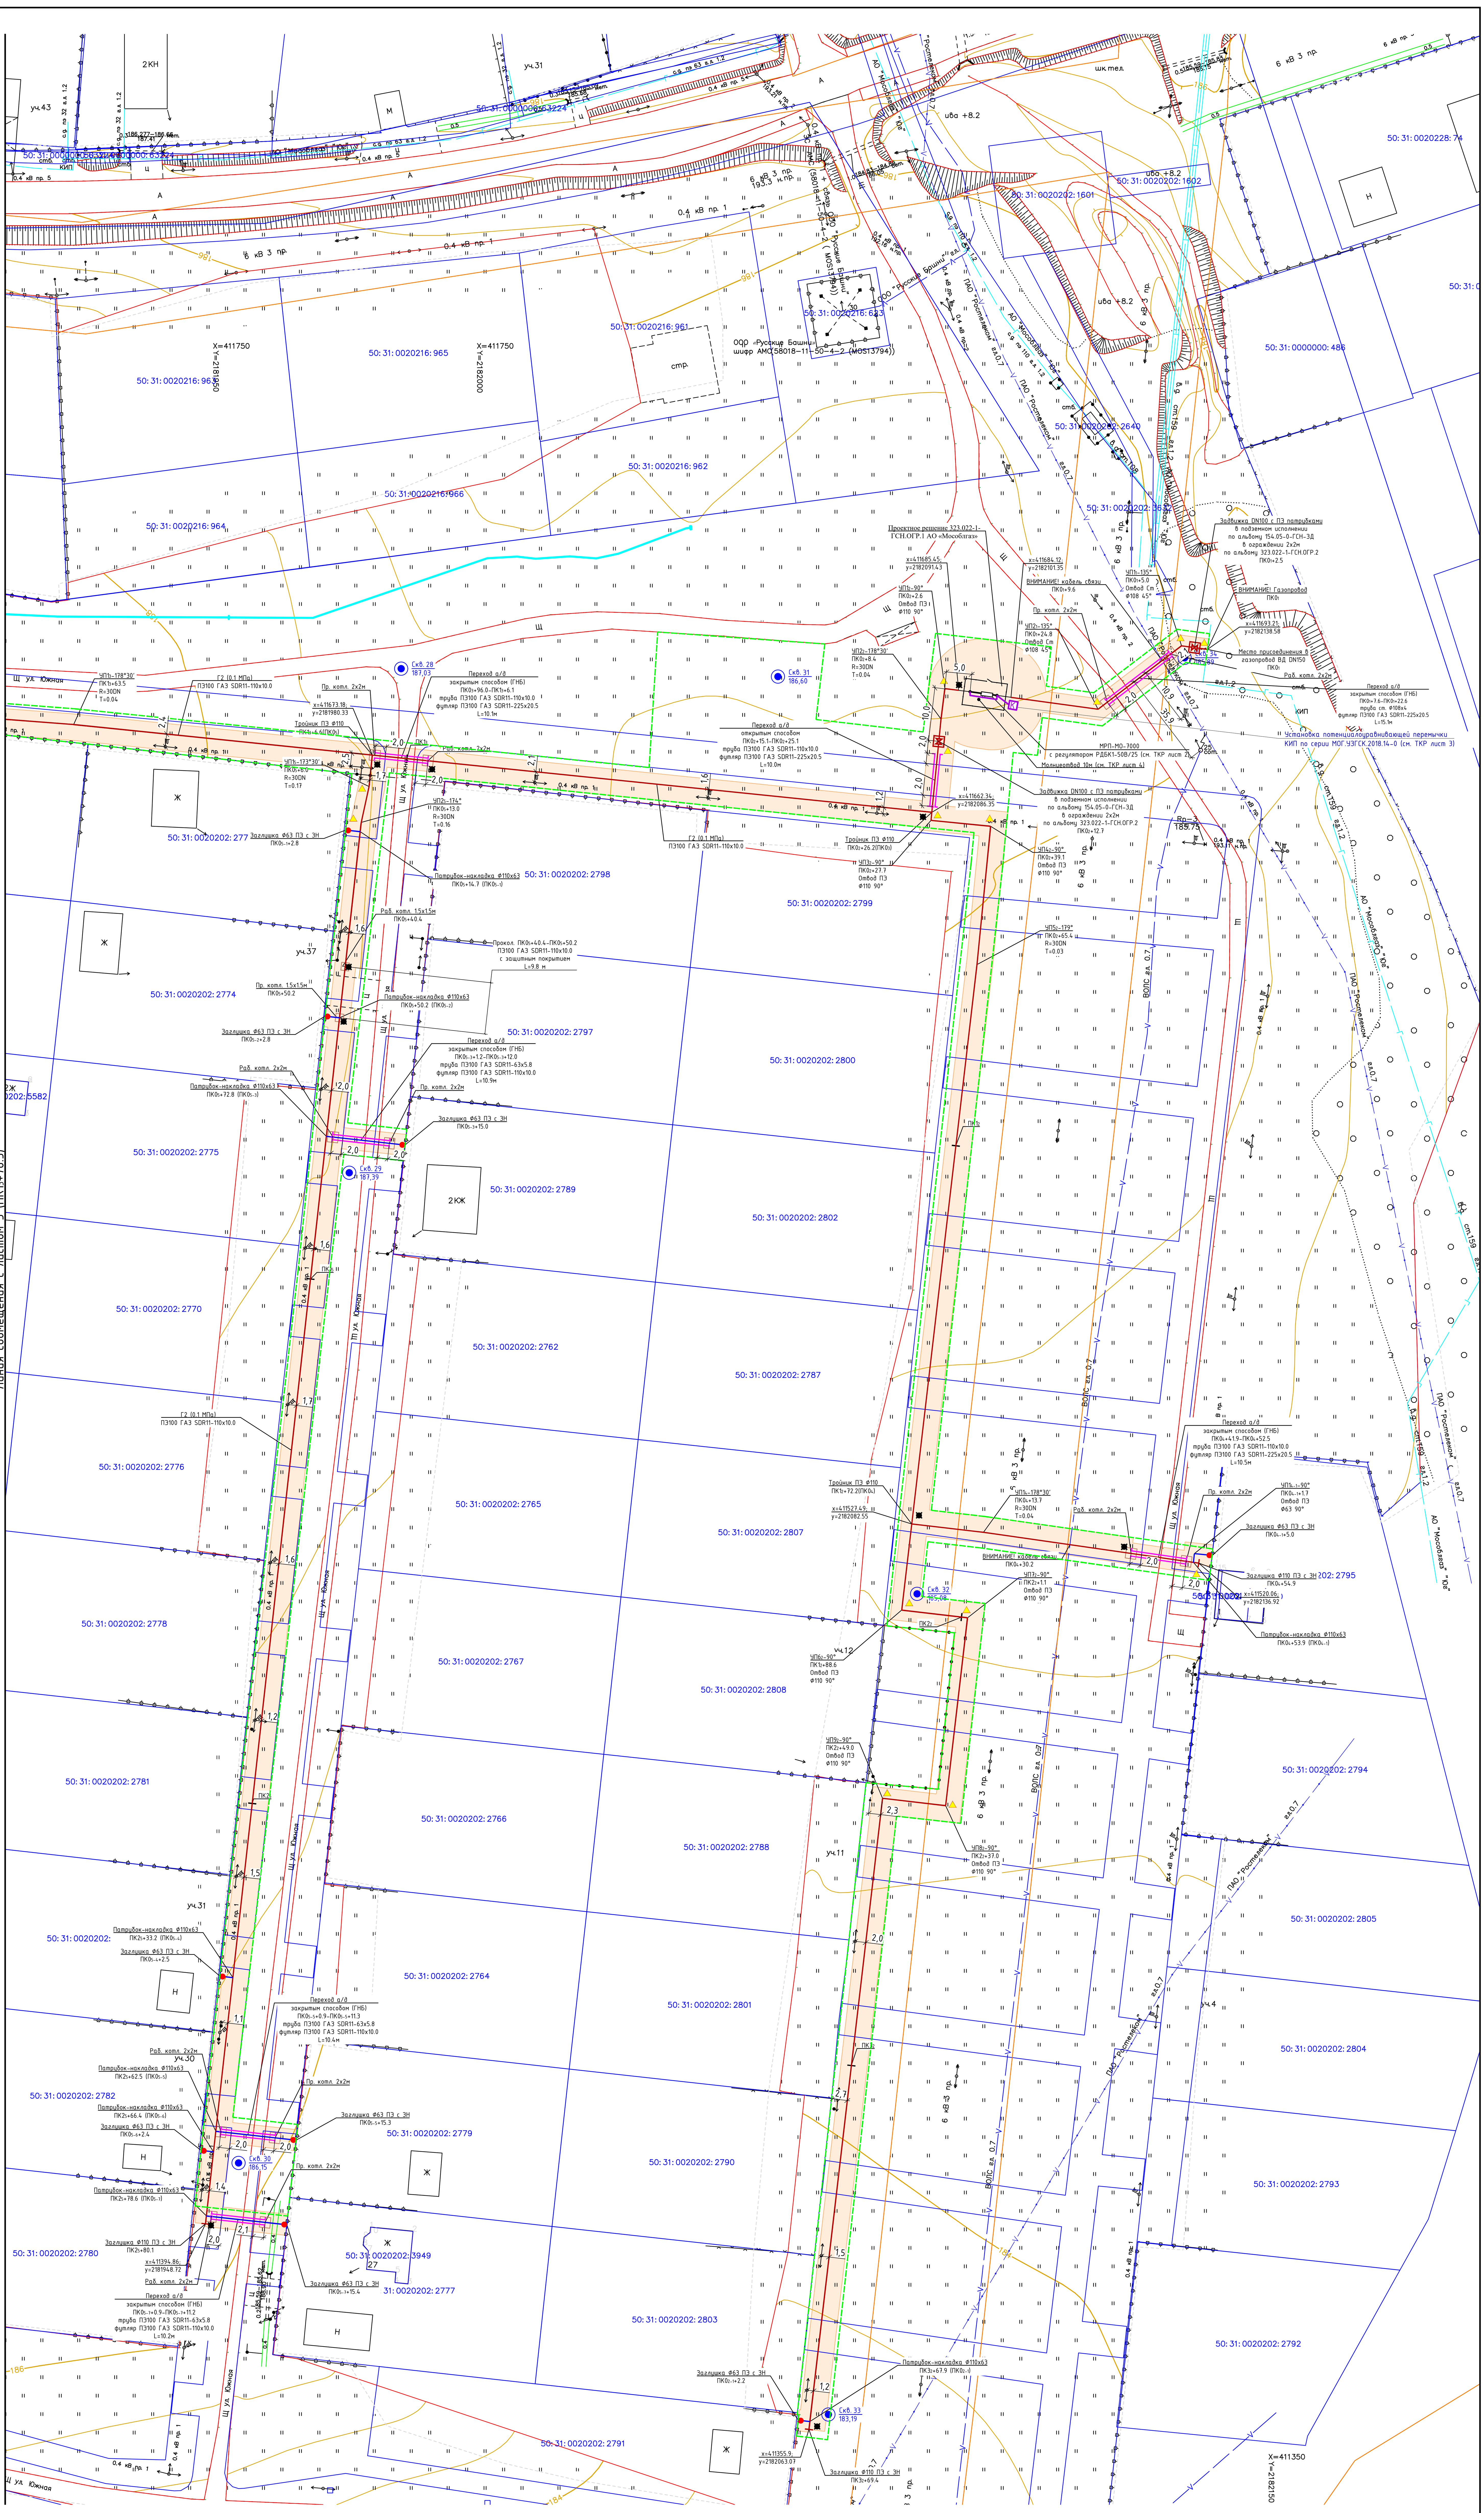

Схема расположения листов

4	3	2

Условные обозначения

- Граница застроенной территории
- Граница незастроенной территории
- Граница кадастрового деления
- Граница охранных зон
- Граница полосы отвода
- Монтажный котлован размером 2х2м
- Участок восстановления дорожного покрытия
- Участок восстановления канавы
- Информационная стойка "Ин"
- Отключающее устройство DN50 на газопроводе-вводе по проектному решению ГУП МО "Мособлгаз" 154.05-0-ГСН.3Д
- Вывод кабеля-спутника в стойку КИП МОГ.УЗГСК.2021.19 АО "Мособлгаз"
- Проектируемый газопровод среднего давления
- Проектируемый газопровод-ввод
- Футляр газопровода
- Контрольная трубка
- ЛЭП напряжением 0,4кВ
- Кабель

Координаты углов

Номер угла	x	y
УП1₁	411693.88	2182133.67
УП2₁	411681.87	2182117.85
УП1₂	411685.78	2182088.82
УП2₂	411680.01	2182088.1
УП3₂	411660.81	2182086.2
УП4₂	411659.69	2182097.5
УП5₂	411633.48	2182094.91
УП6₂	411511.16	2182080.64
УП7₂	411509.7	2182093.12
УП8₂	411474.1	2182088.96
УП9₂	411475.5	2182077.01
УП1₃	411678.97	2181923.72
УП1₄	411525.9	2182096.14
УП1₅	411667.23	2181979.72
УП2₅	411660.42	2181978.23

Пикетаж арматуры и координаты заглушек газопроводов-отводов (ГО)

Индекс ГО	ПК арматуры	Координаты заглушки	
		x	y
2-1	ПК0₂₋₁+1.7	411357.64	2182061.03
4-1	ПК0₄₋₁+4.6	411521.51	2182139.46
5-1	ПК0₅₋₁+2.3	411658.97	2181975.26
5-2	ПК0₅₋₂+2.3	411623.71	2181971.35
5-3	ПК0₅₋₃+14.5	411599.29	2181986.52
5-4	ПК0₅₋₄+2.0	411441.8	2181951.46
5-5	ПК0₅₋₅+14.8	411410.71	2181965.88
5-6	ПК0₅₋₆+1.9	411408.77	2181947.88

1. Охранная зона газопроводов-вводов составляет 2м с каждой стороны от оси газопровода
2. Охранная зона распределительного газопровода составляет 3 метра от газопровода со стороны провода и 2 метра – с противоположной стороны
3. Полоса отвода Г2, Г4 составляет 6м
4. Опознавательные знаки установить на опознавательные столбы (стойки типа "Ин") или другие постоянные ориентиры.

Взам. инв. N | Подпись и дата | Инв. N подл.

Изм.	Кол.уч.	Лист	№ док.	Подпись	Дата
Разработал	Разиньков				
Проверил					
Н.контр.					

XXXX-ППО.ГЧ

«Газификация д. Панино» городского округа Чехов Московской области

Проект полосы отвода

Стадия	Лист	Листов
П	2	

План газопровода
ПК0₁-ПК0₁+41.5; ПК0₂-ПК3₂+69.4; ПК0₃-ПК1₃+76.5;
ПК0₄-ПК0₄+54.9; ПК0₅-ПК2₅+80.1.
М1:500.

Формат А2х3