


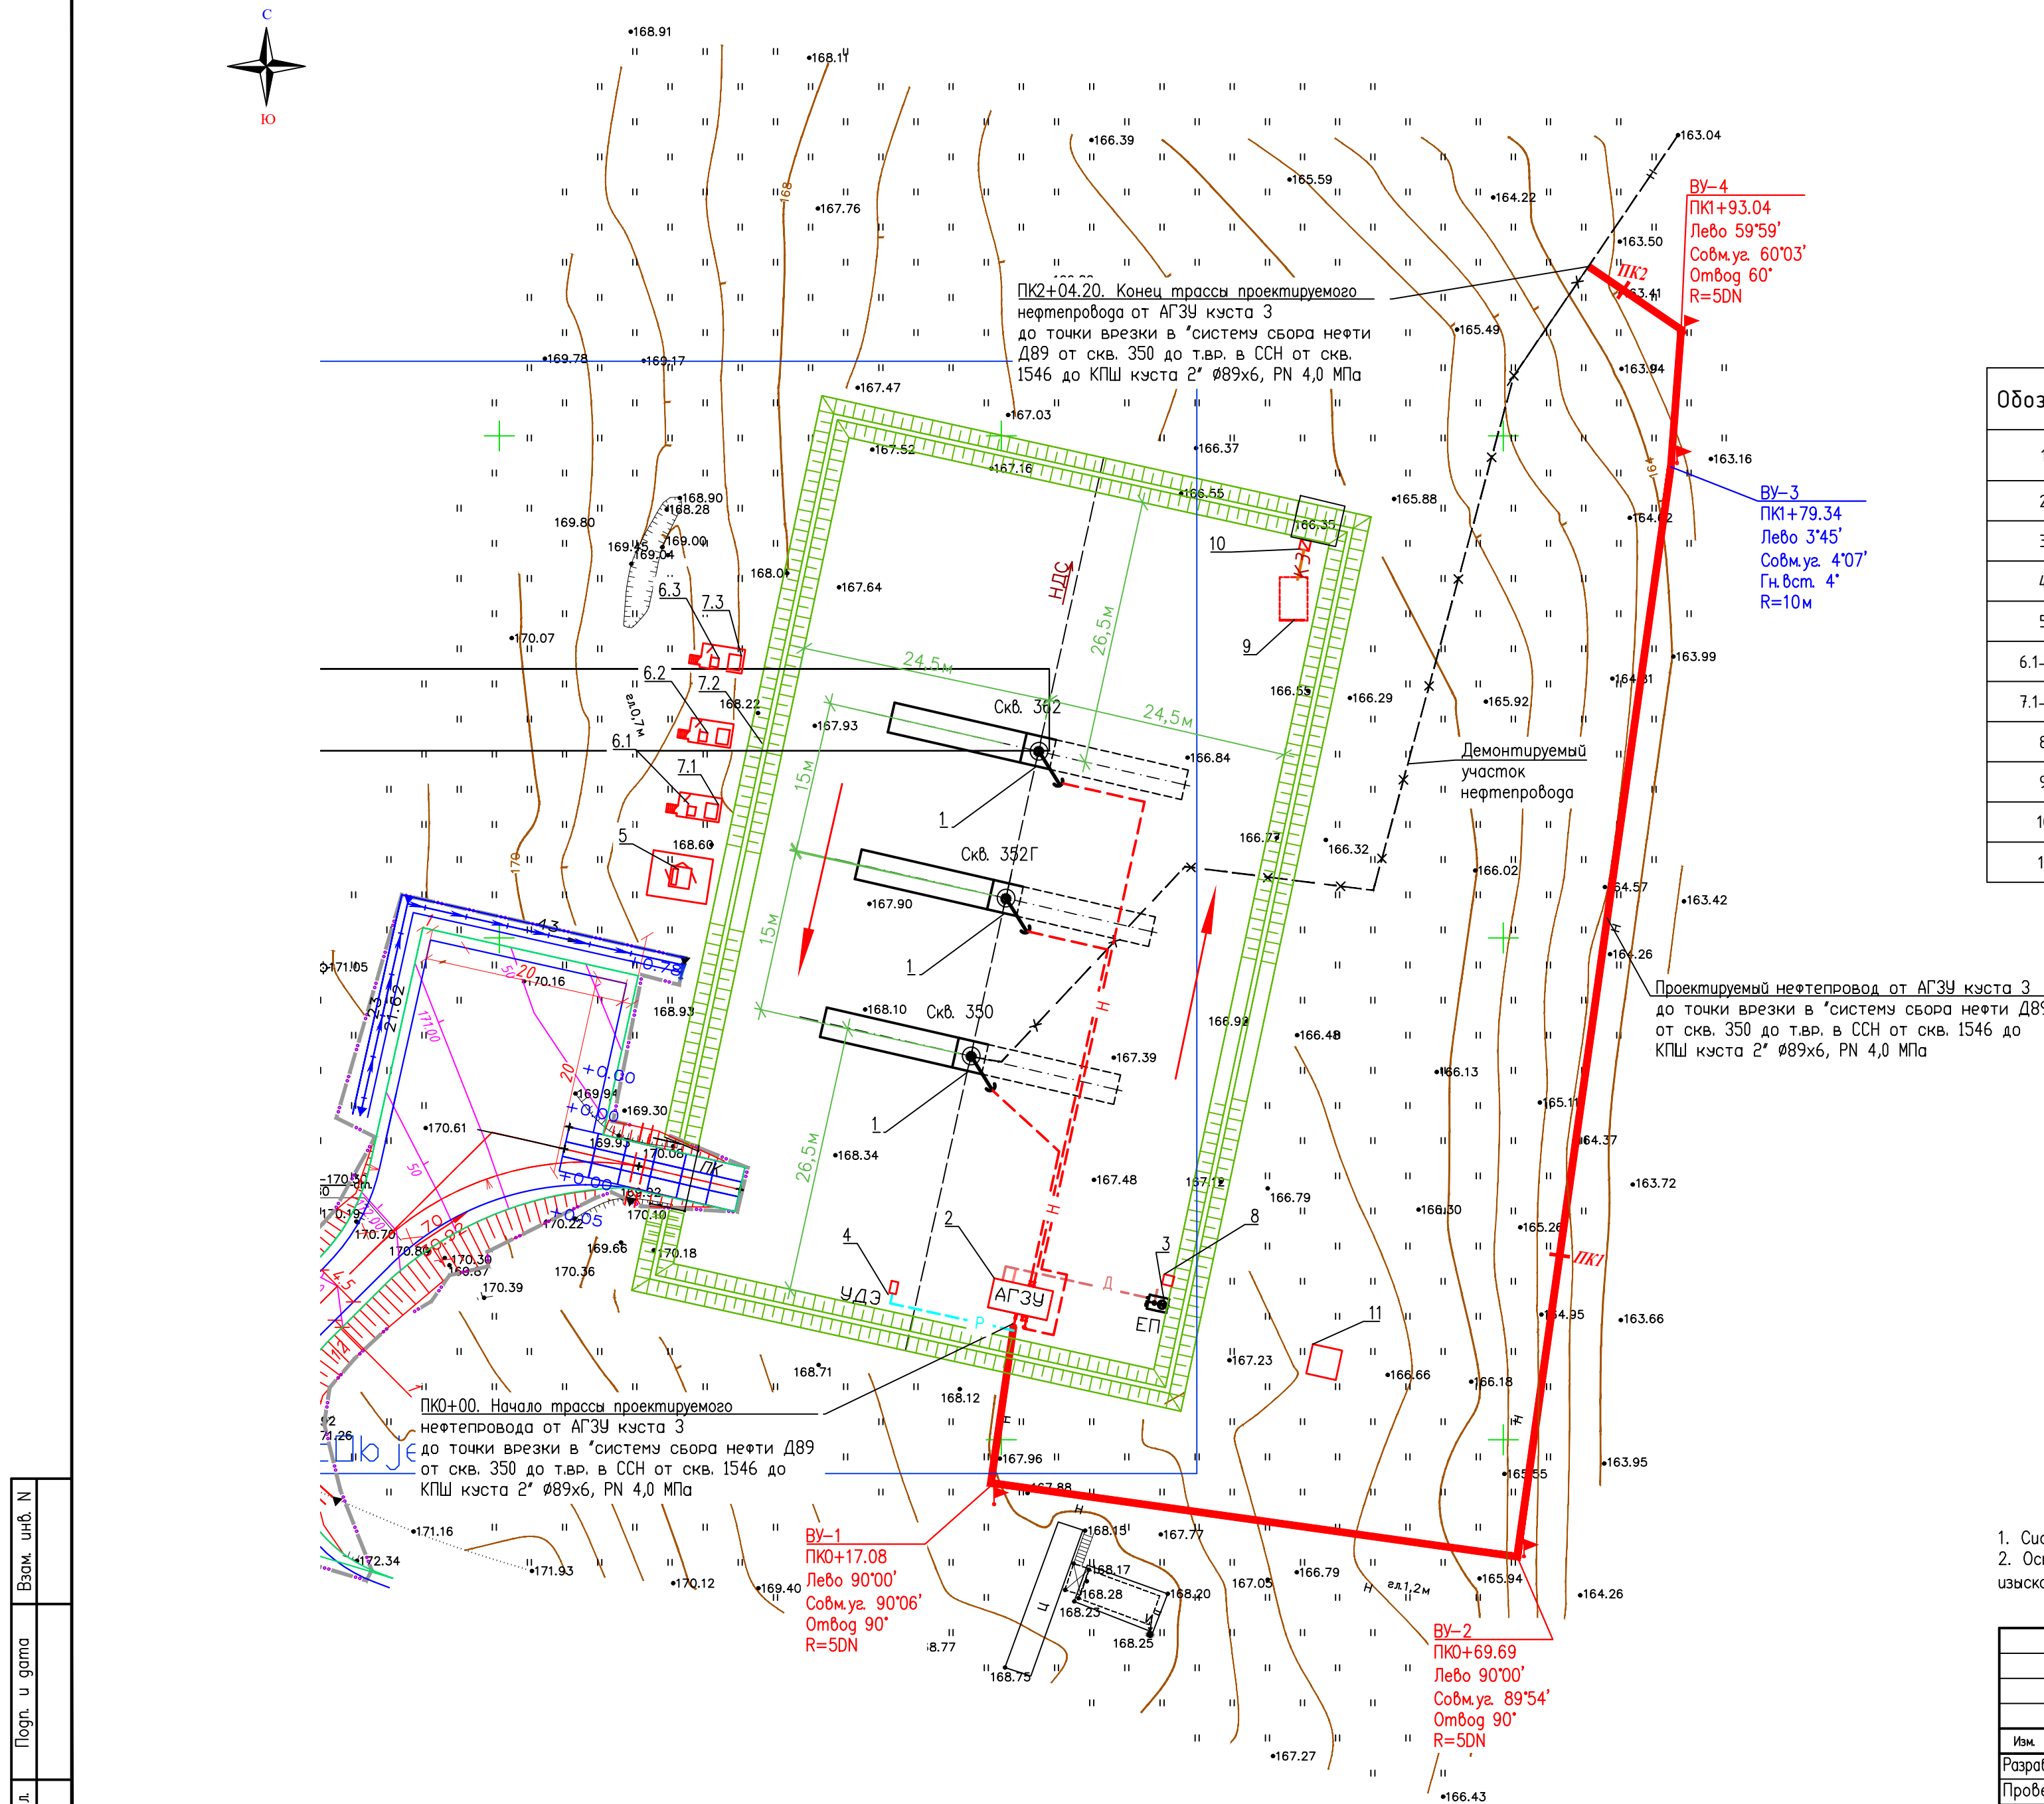

Экспликация оборудования

Обознач.	Наименование	Кол-во	Примечание
1	Добывающая скважина, оборудованная ЭЦН	3	
2	Автоматизированная групповая замерная установка	1	ОЗНА-Массомер-8
3	Емкость производственных стоков, V=3м3	1	ЕП 3-1400
4	Установка дозирующая электронасосная УДЭ	1	УДЭ
5	КТП		
6.1-6.3	Трансформатор для ЭЦН		
7.1-7.3	Станция управления для ЭЦН		
8	Молниеотвод		
9	Емкость ливневых стоков ЕП 12,5		
10	Дождеприемный колодец (ДП1)		
11	Блок аппаратный		

Условные обозначения

- Н — Проектируемый выкидной коллектор
- Проектируемый нефтесборный трубопровод
- Д — Проектируемый трубопровод дренажа
- Р — Проектируемый реагентопровод
- Н — Существующий нефтепровод
- X — Демонтируемый нефтепровод
- Клапан обратный фланцевый
- Задвижка фланцевая
- Знак опознавательный

- 1. Система высот — Балтийская.
- 2. Основой для составления чертежа служили материалы комплексных инженерных изысканий ООО "Трансэнергострой", выполненных в сентябре-декабре 2016г.

						XXXXXXXX-ИОС7.1.ПРЛБ			
						Обустройство Пограничного нефтяного месторождения. Второй этап.			
Изм.	Кол-во	Лист	№ок	Подпись	Дата	Нефтесборные сети	Стадия	Лист	Листов
Разработал							П		1
Проверил						План куста №3. План нефтепровода от АГЗУ куста №3 до т. вр. в "систему сбора нефти Д89 от скважины №350 до точки врезки в ССН от скважины №1546 до КПП куста №2". М1:500			
Н.контр.									
ГИП									