


План М1:100

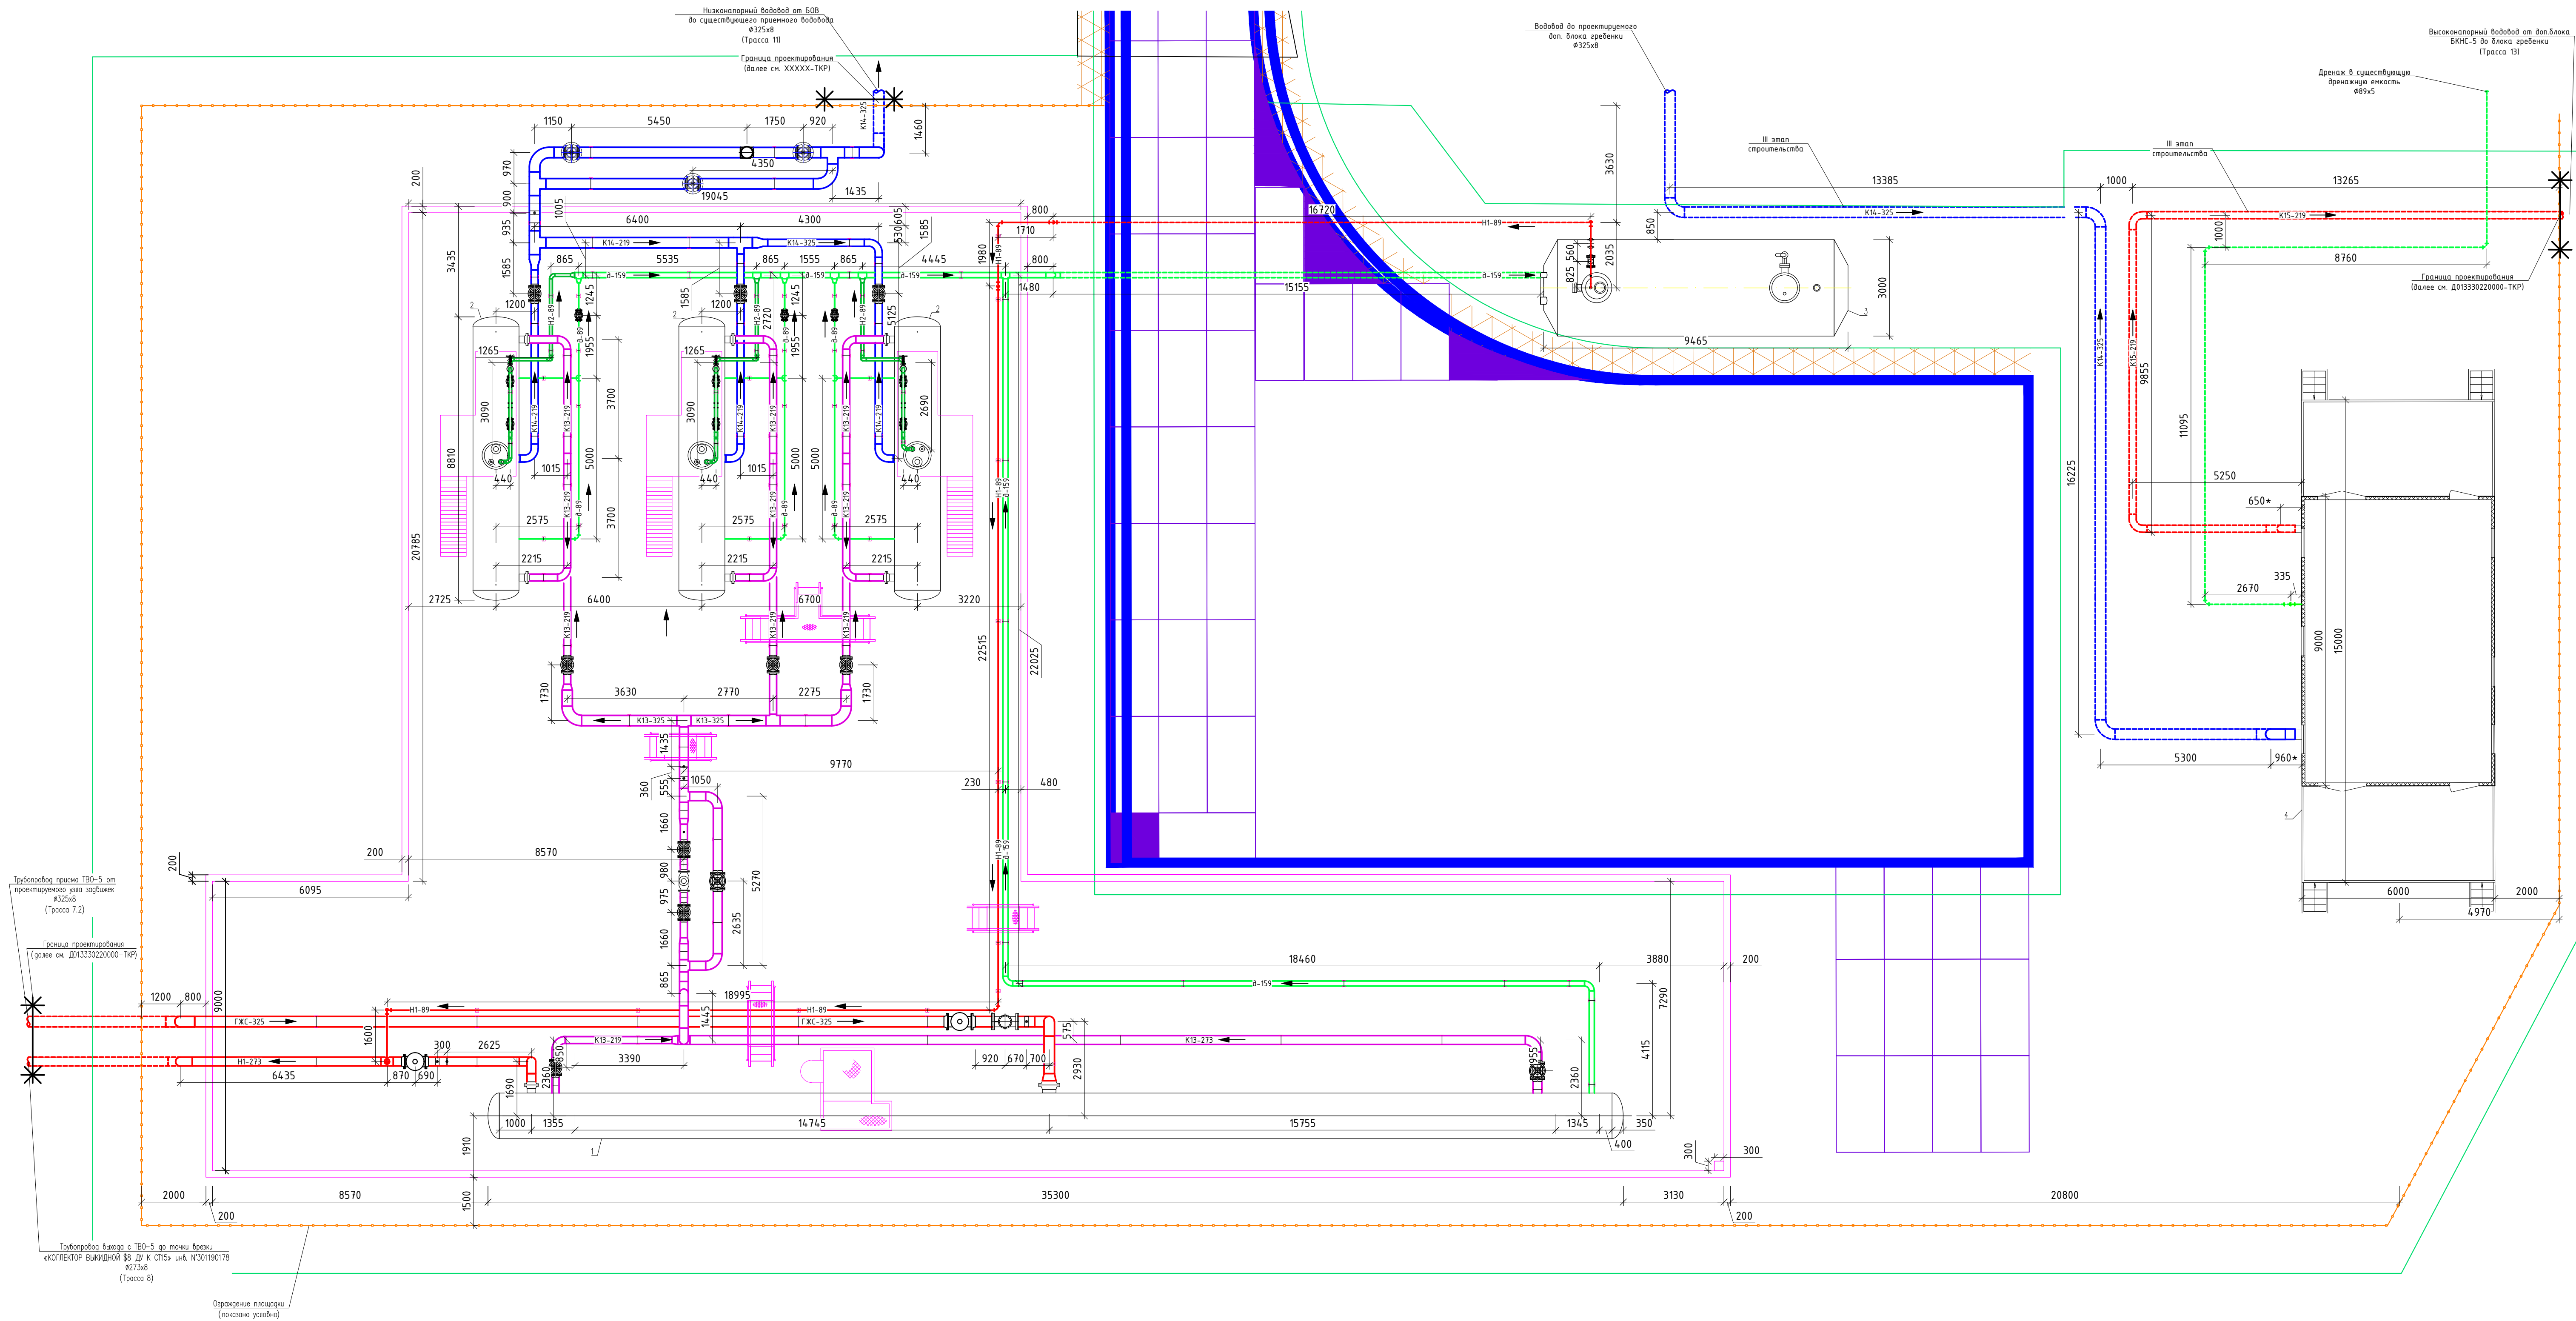

XXXXXXX-ИЛ06.ГЧ					
Обустройство Вятской площадки Арланского нефтяного месторождения. ТВО-5, расширение БКНС-5					
Изм.	Колуч.	Лист	№ док.	Подпись	Дата
Разработал					
Проверил					
Н.контр.					
Технологические решения				Стадия	Лист
				П	3
План площадки ТВО-5. М1:100.				Листов	

Экспликация зданий и сооружений			
	Наименование	Кол-во	Примечание
1	ТВО	1	II Этап стр.
2	БОВ (фильтры потоковые-3шт)	1	II Этап стр.
3	Дренажная емкость	1	II Этап стр.
4	Дополнительный блок БКНС	1	III Этап стр.

Примечание:
1. Строительная часть показана условно.
2. Смотреть совместно с листом 2.